


DETALHE  
ENTRADA DE ENERGIA

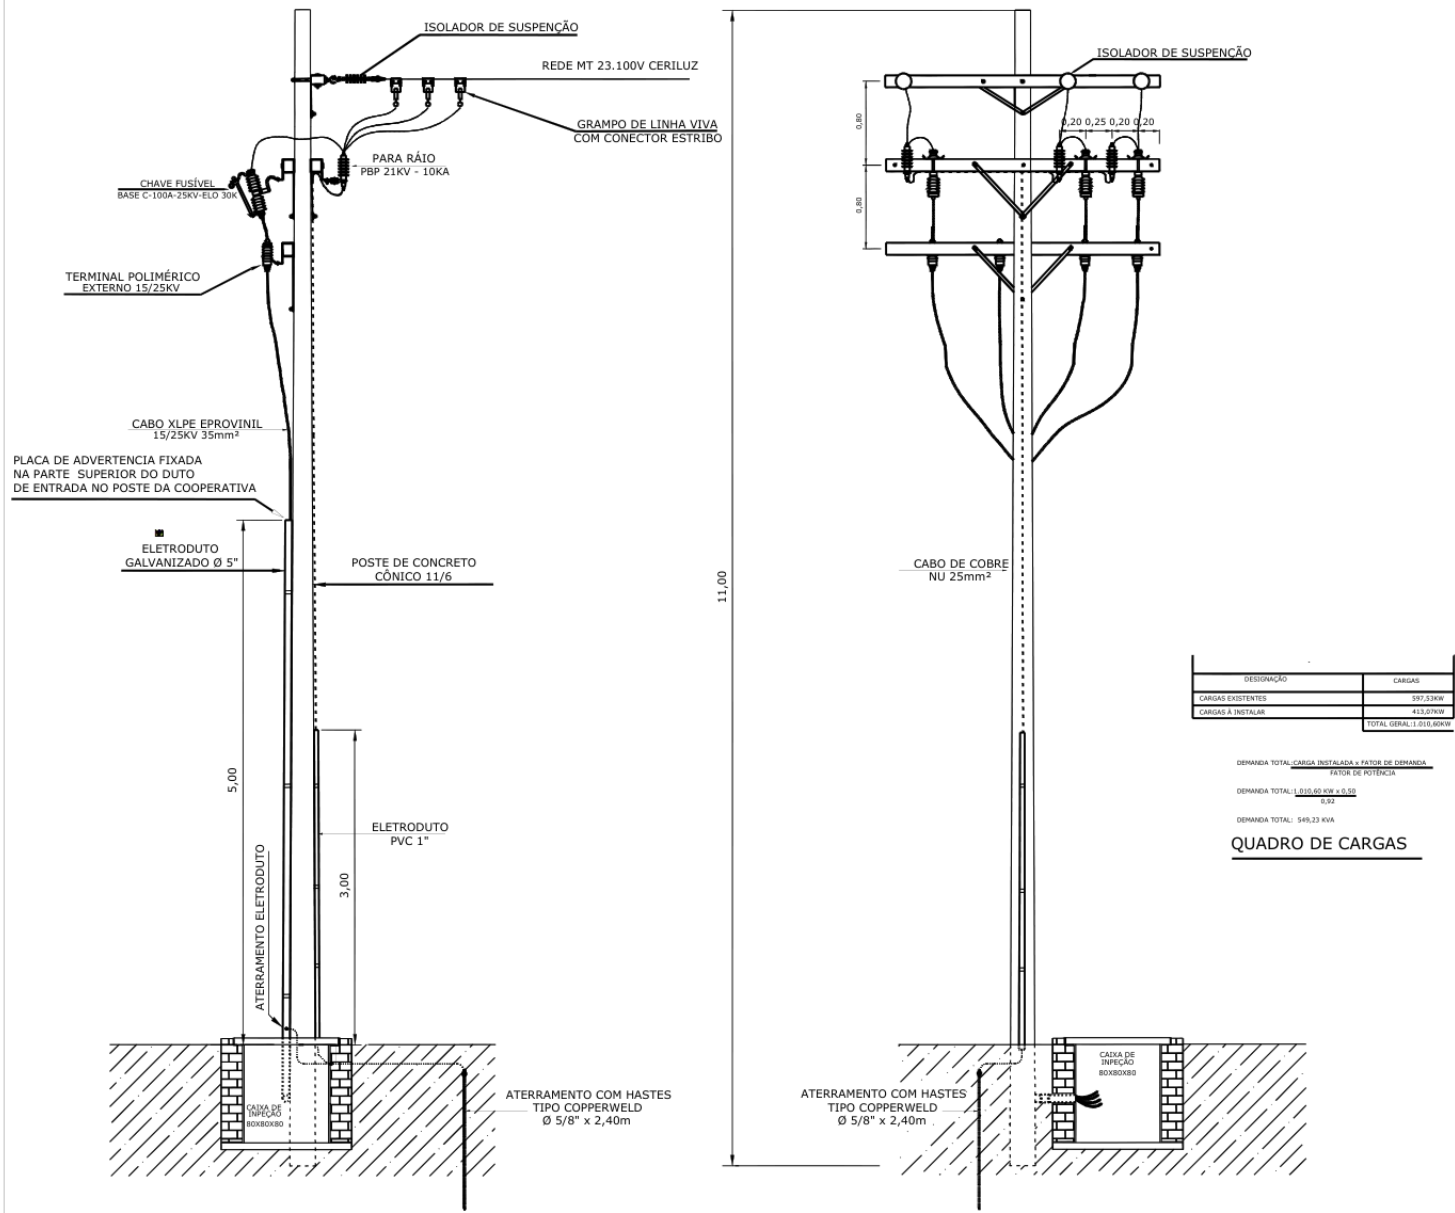


RAMAL DE ENTRADA MT  
ESCALA - 1:25




NOTA:  
SERÃO FIXADAS PLACAS DE ADVERTÊNCIA ("CUIDADO - RISCO DE CHOQUE ELÉTRICO - GERAÇÃO PRÓPRIA") NOS SEGUINTE LOCAIS:  
-POSTE DE ENERGIA (ENTRADA TIPO SUBTERRÂNEA).  
-PORTA DE ENTRADA DA CABINE DE MEDIÇÃO;  
-TAMPA DA CAIXA DE MEDIÇÃO;


# DETALHE SUBESTAÇÃO

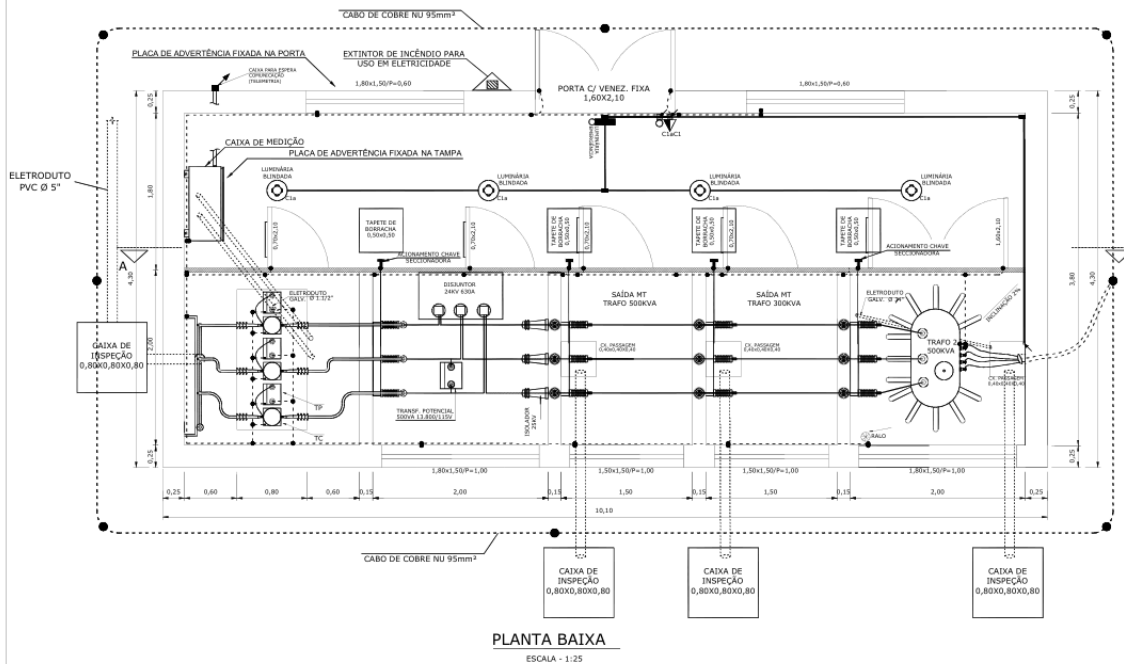

MEDIÇÃO INDIRETA EM MT

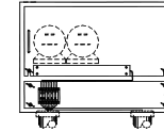


DIMENSÕES CAIXA MEDIÇÃO

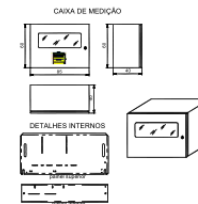


NOTA:  
SERÃO FIXADAS PLACAS DE ADVERTÊNCIA ("CUIDADO - RISCO DE CHOQUE ELÉTRICO - GERAÇÃO PRÓPRIA") NOS SEGUINTE LOCAIS:  
-POSTE DE ENERGIA (ENTRADA TIPO SUBTERRÂNEA).  
-PORTA DE ENTRADA DA CABINE DE MEDIÇÃO;  
-TAMPA DA CAIXA DE MEDIÇÃO;

NOTAS:


- 1- AS JANELAS E A PORTA DEVEM SER METÁLICAS COM VENEZIANAS FIXAS.
- 2- A PORTA PRINCIPAL DEVERÁ POSSUIR FECHADURA TIPO PADRÃO CPFL.
- 3- TODAS AS PARTES METÁLICAS DEVERÃO SER ATERRADAS COM CABO 35mm<sup>2</sup>.
- 4- AS PAREDES INTERNAS DA CABINE DEVERÃO SER ALISADAS COM ARGAMASSA FINA E APÓS PINTADAS COM TINTA DE BOA QUALIDADE COR BRANCA.
- 5- A LAJE DO PISO DEVERÁ POSSUIR ESPESURA DE 0,12m.
- 6- A CHAVE SECCIONADORA DEVERÁ PERMITIR, QUANDO DA SUA ABERTURA UMA EXCURSÃO MÍNIMA DE 22cm, ENTRE A PARTE MÓVEL E A BORNE ENERGIZADO.
- 7- AS CAIXAS DE PASSAGEM EXTERNAS DEVERÃO POSSUIR TAMPA COM DISPOSITIVO PARA LACRE.
- 8- TODAS AS CHAVES SECCIONADORAS DEVERÃO SER INTERTRAVADAS COM O DISJUNTOR DE MT. DEVE POSSUIR UM DISPOSITIVO DE TRAVAMENTO MECÂNICO PARA IMPEDIR A SUA ABERTURA E FECHAMENTO ACIDENTAL.
- 9- AS PAREDES DA CABINE DEVERÃO SER CONSTRUÍDAS COM TIDULO MACIÇO E TETO DE CONCRETO ARMADO.
- 10- A RESISTÊNCIA MÁXIMA DA TERRA NÃO DEVE ULTRAPASSAR 10 OHMS EM QUALQUER ÉPOCA DO ANO.
- 11- AS DIMENSÕES INDICADAS SÃO EM METROS.

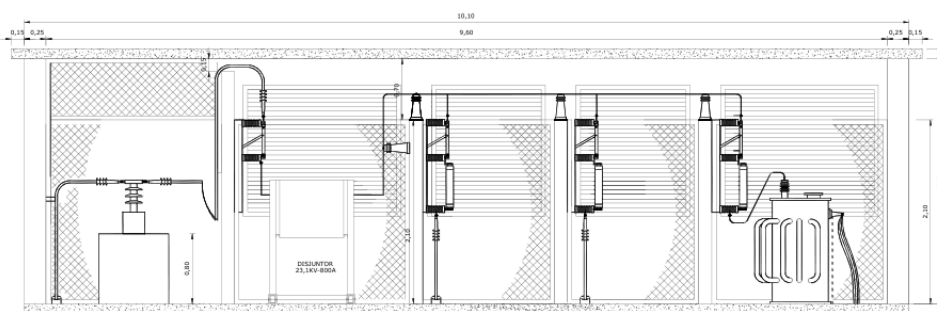

CORTE A - A'  
ESCALA - 1:25

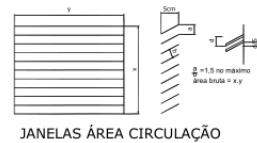

JANELAS ÁREA CIRCULAÇÃO

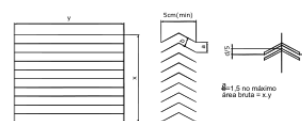

JANELAS COMPARTIMENTO DE MT



# DIAGRAMA UNIFILAR

