




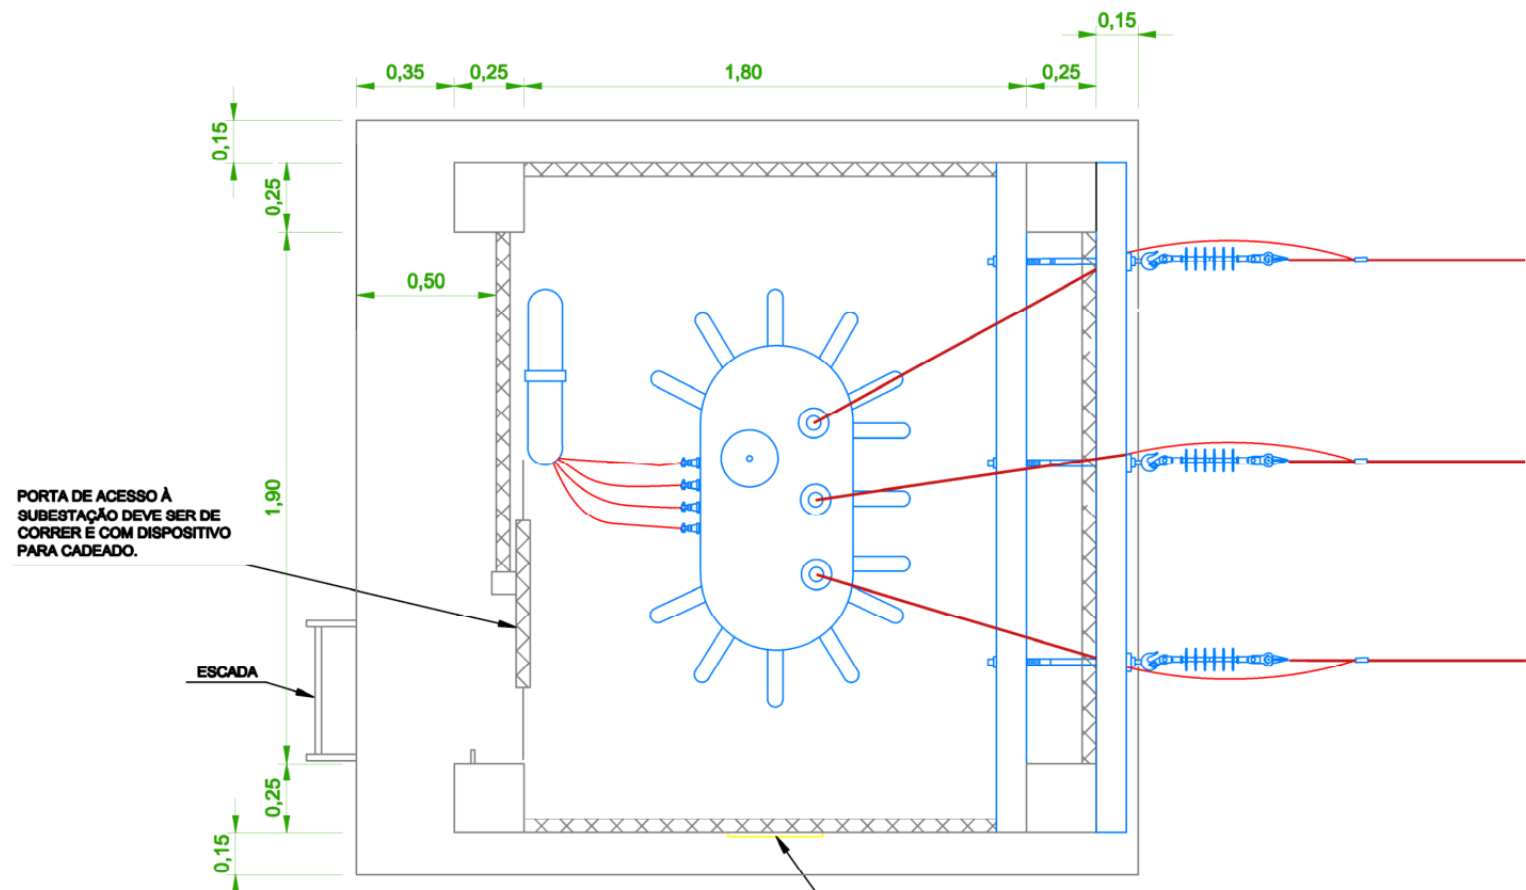


**PLANTA BAIXA
PAVIMENTO SUPERIOR**
ESCALA - 1:25

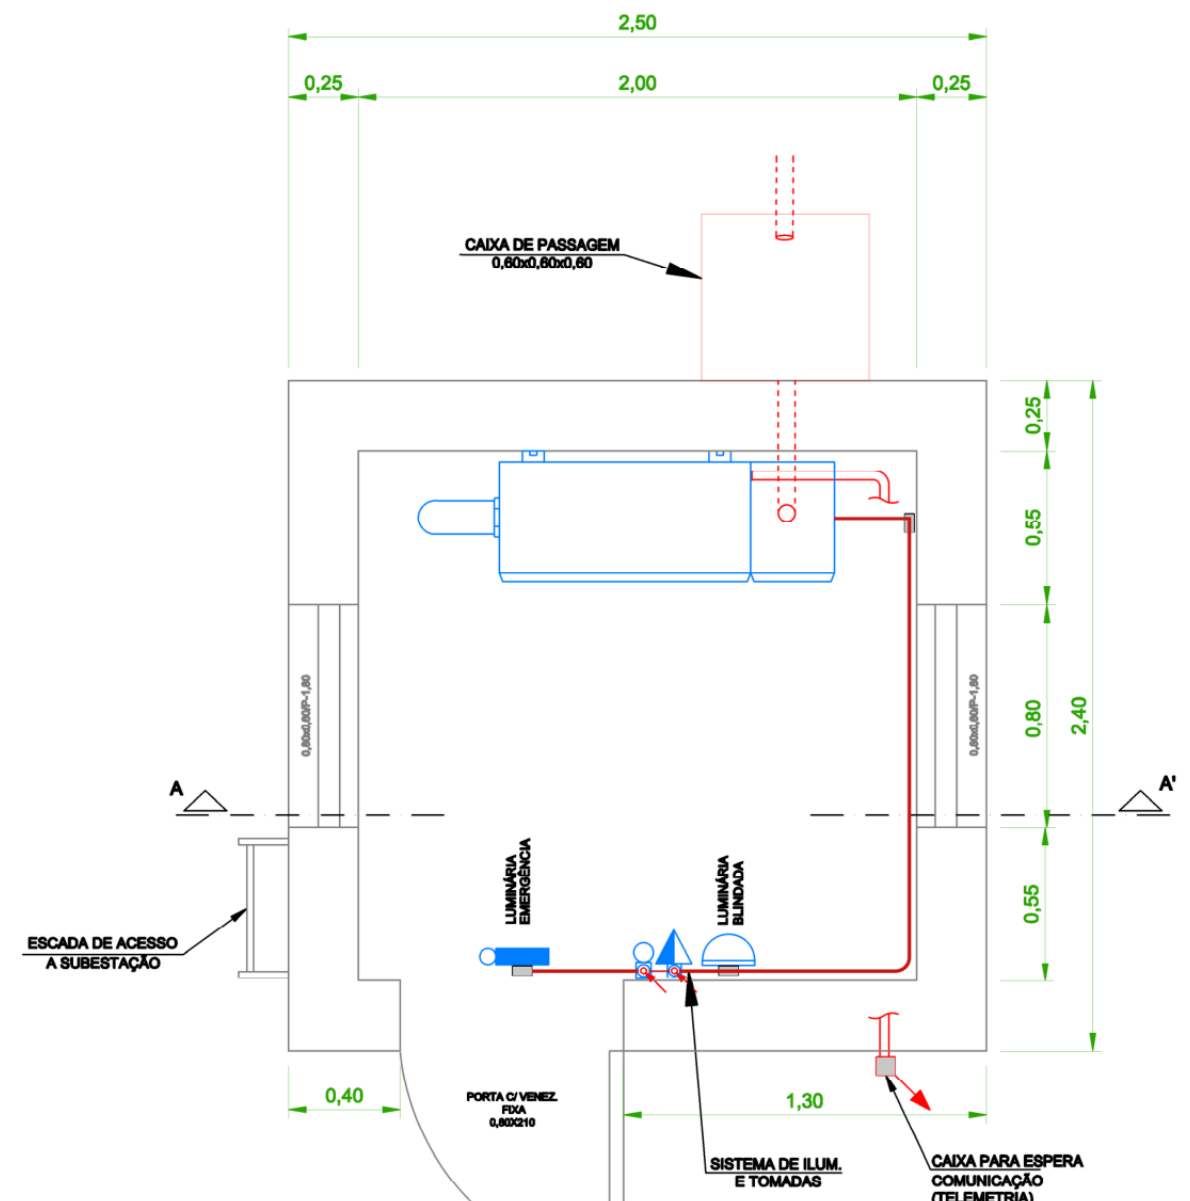


**PLANTA BAIXA
PAVIMENTO INFERIOR**
ESCALA - 1:25

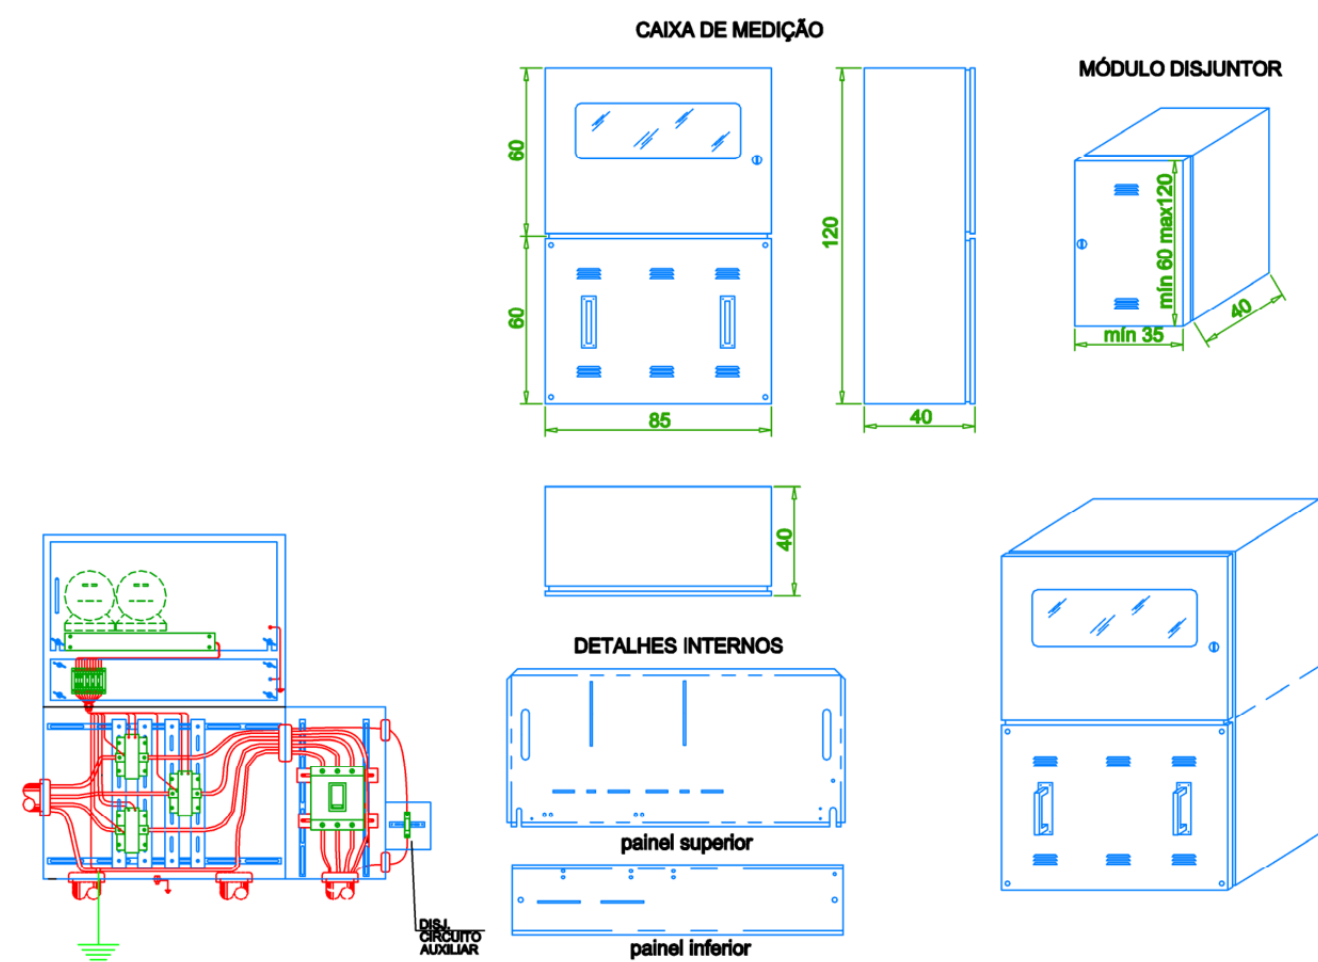


CAIXA DE MEDIÇÃO INDIRETA EM BT
ESCALA - 1:25

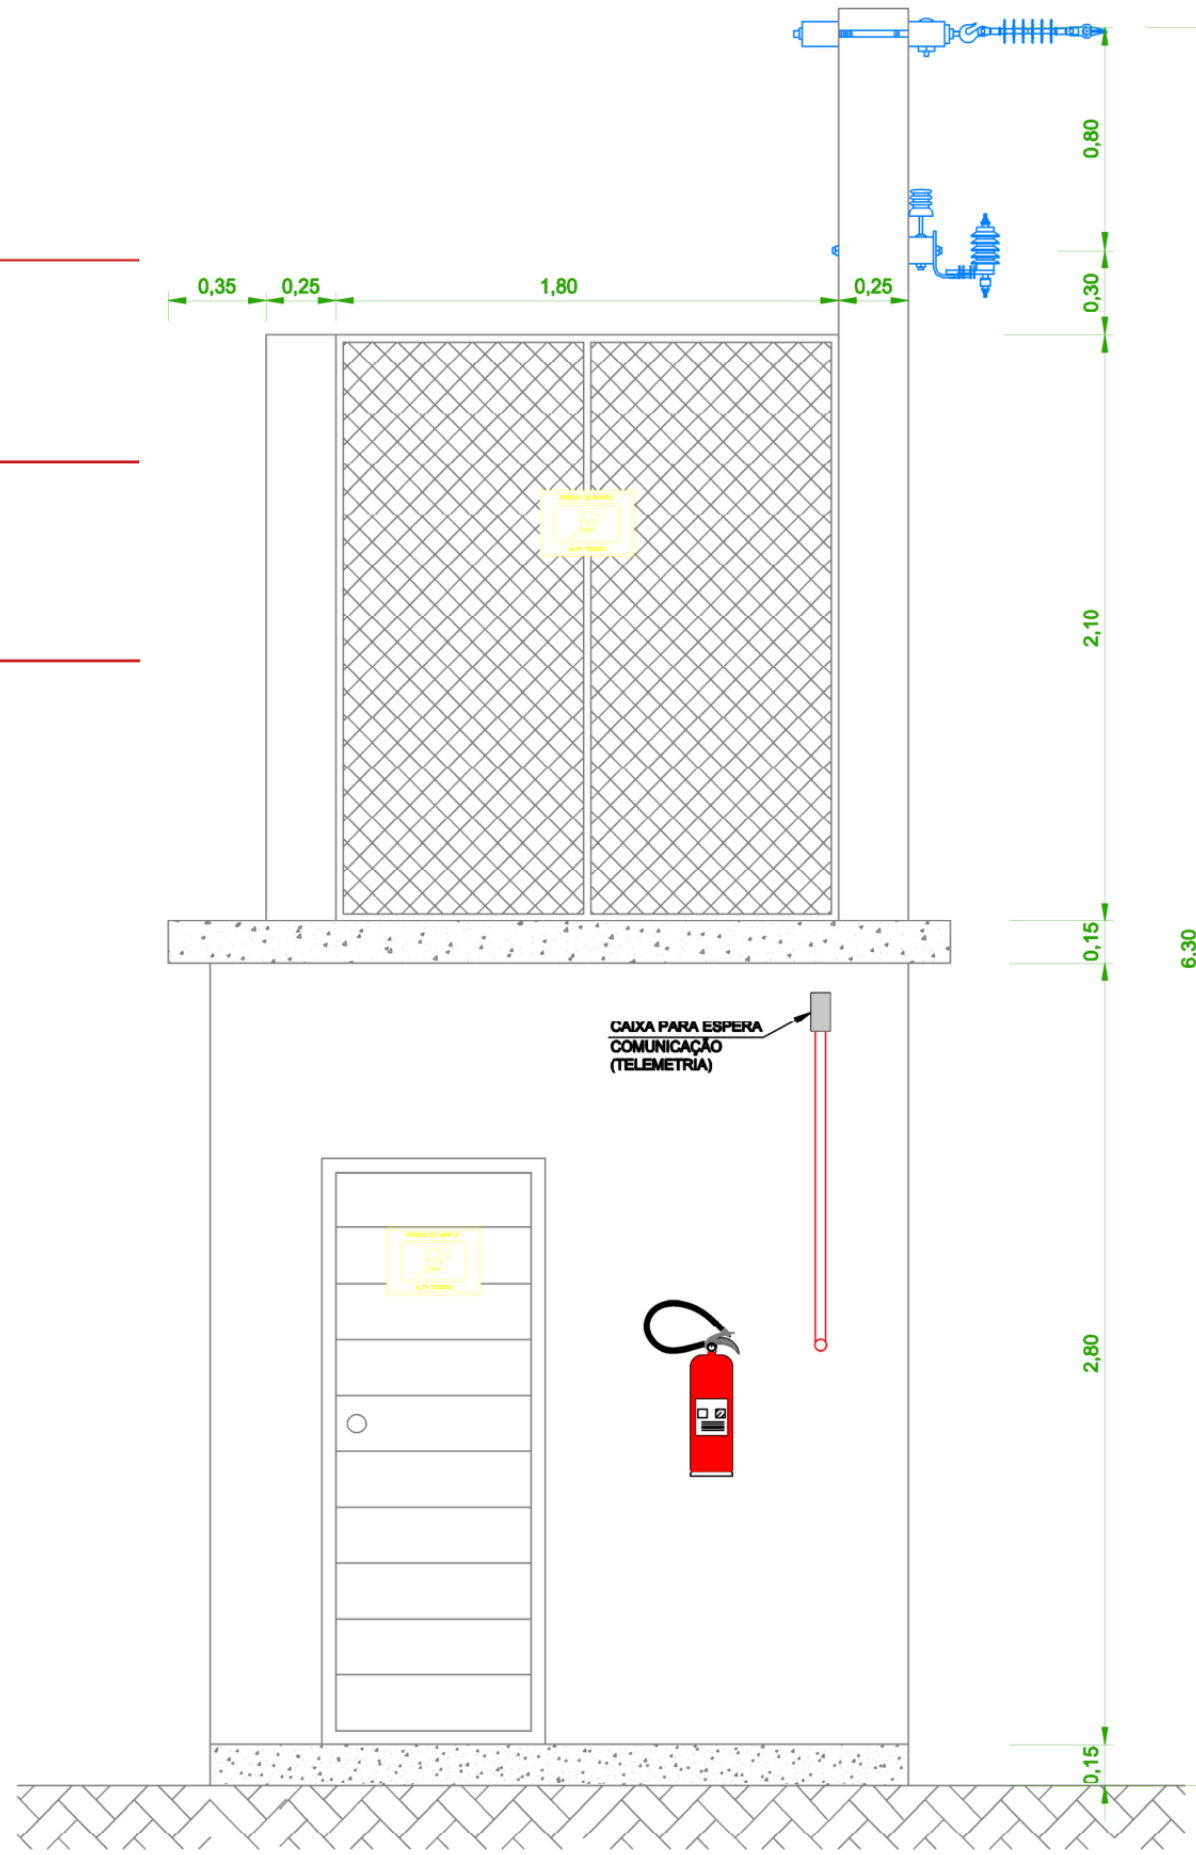


VISTA FRONTAL (FACHADA)
ESCALA - 1:25

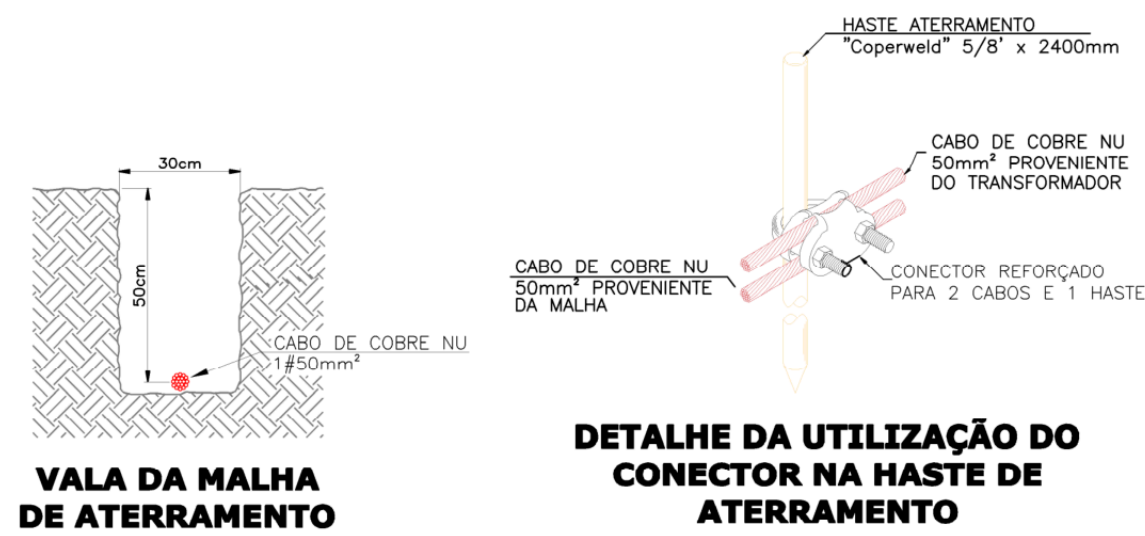

**DETALHE DA UTILIZAÇÃO DO
CONECTOR NA HASTE DE
ATERRAMENTO**

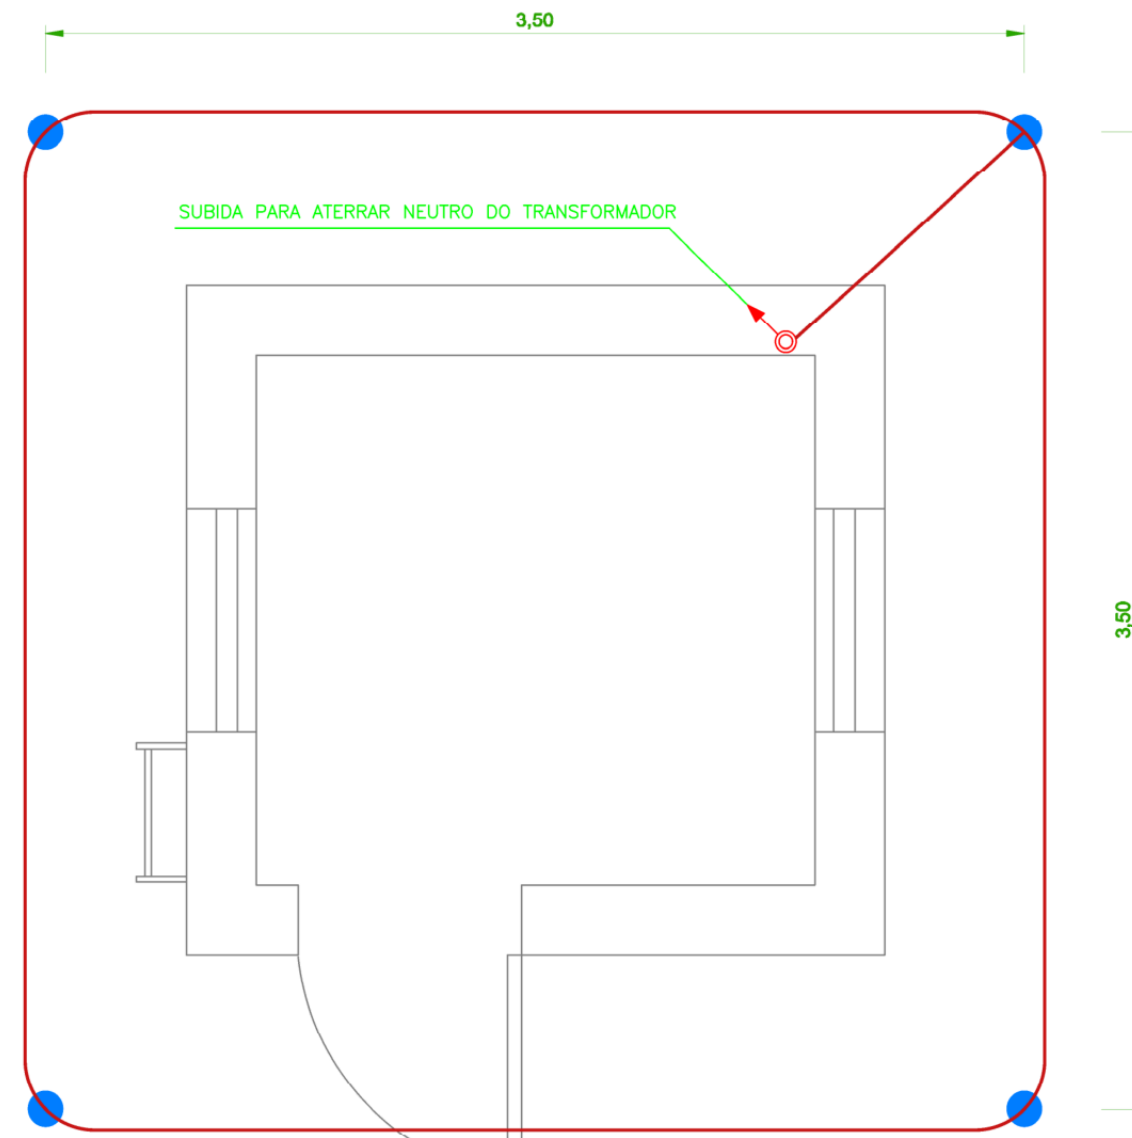


DETALHE DO ATERRAMENTO
ESCALA - 1:25

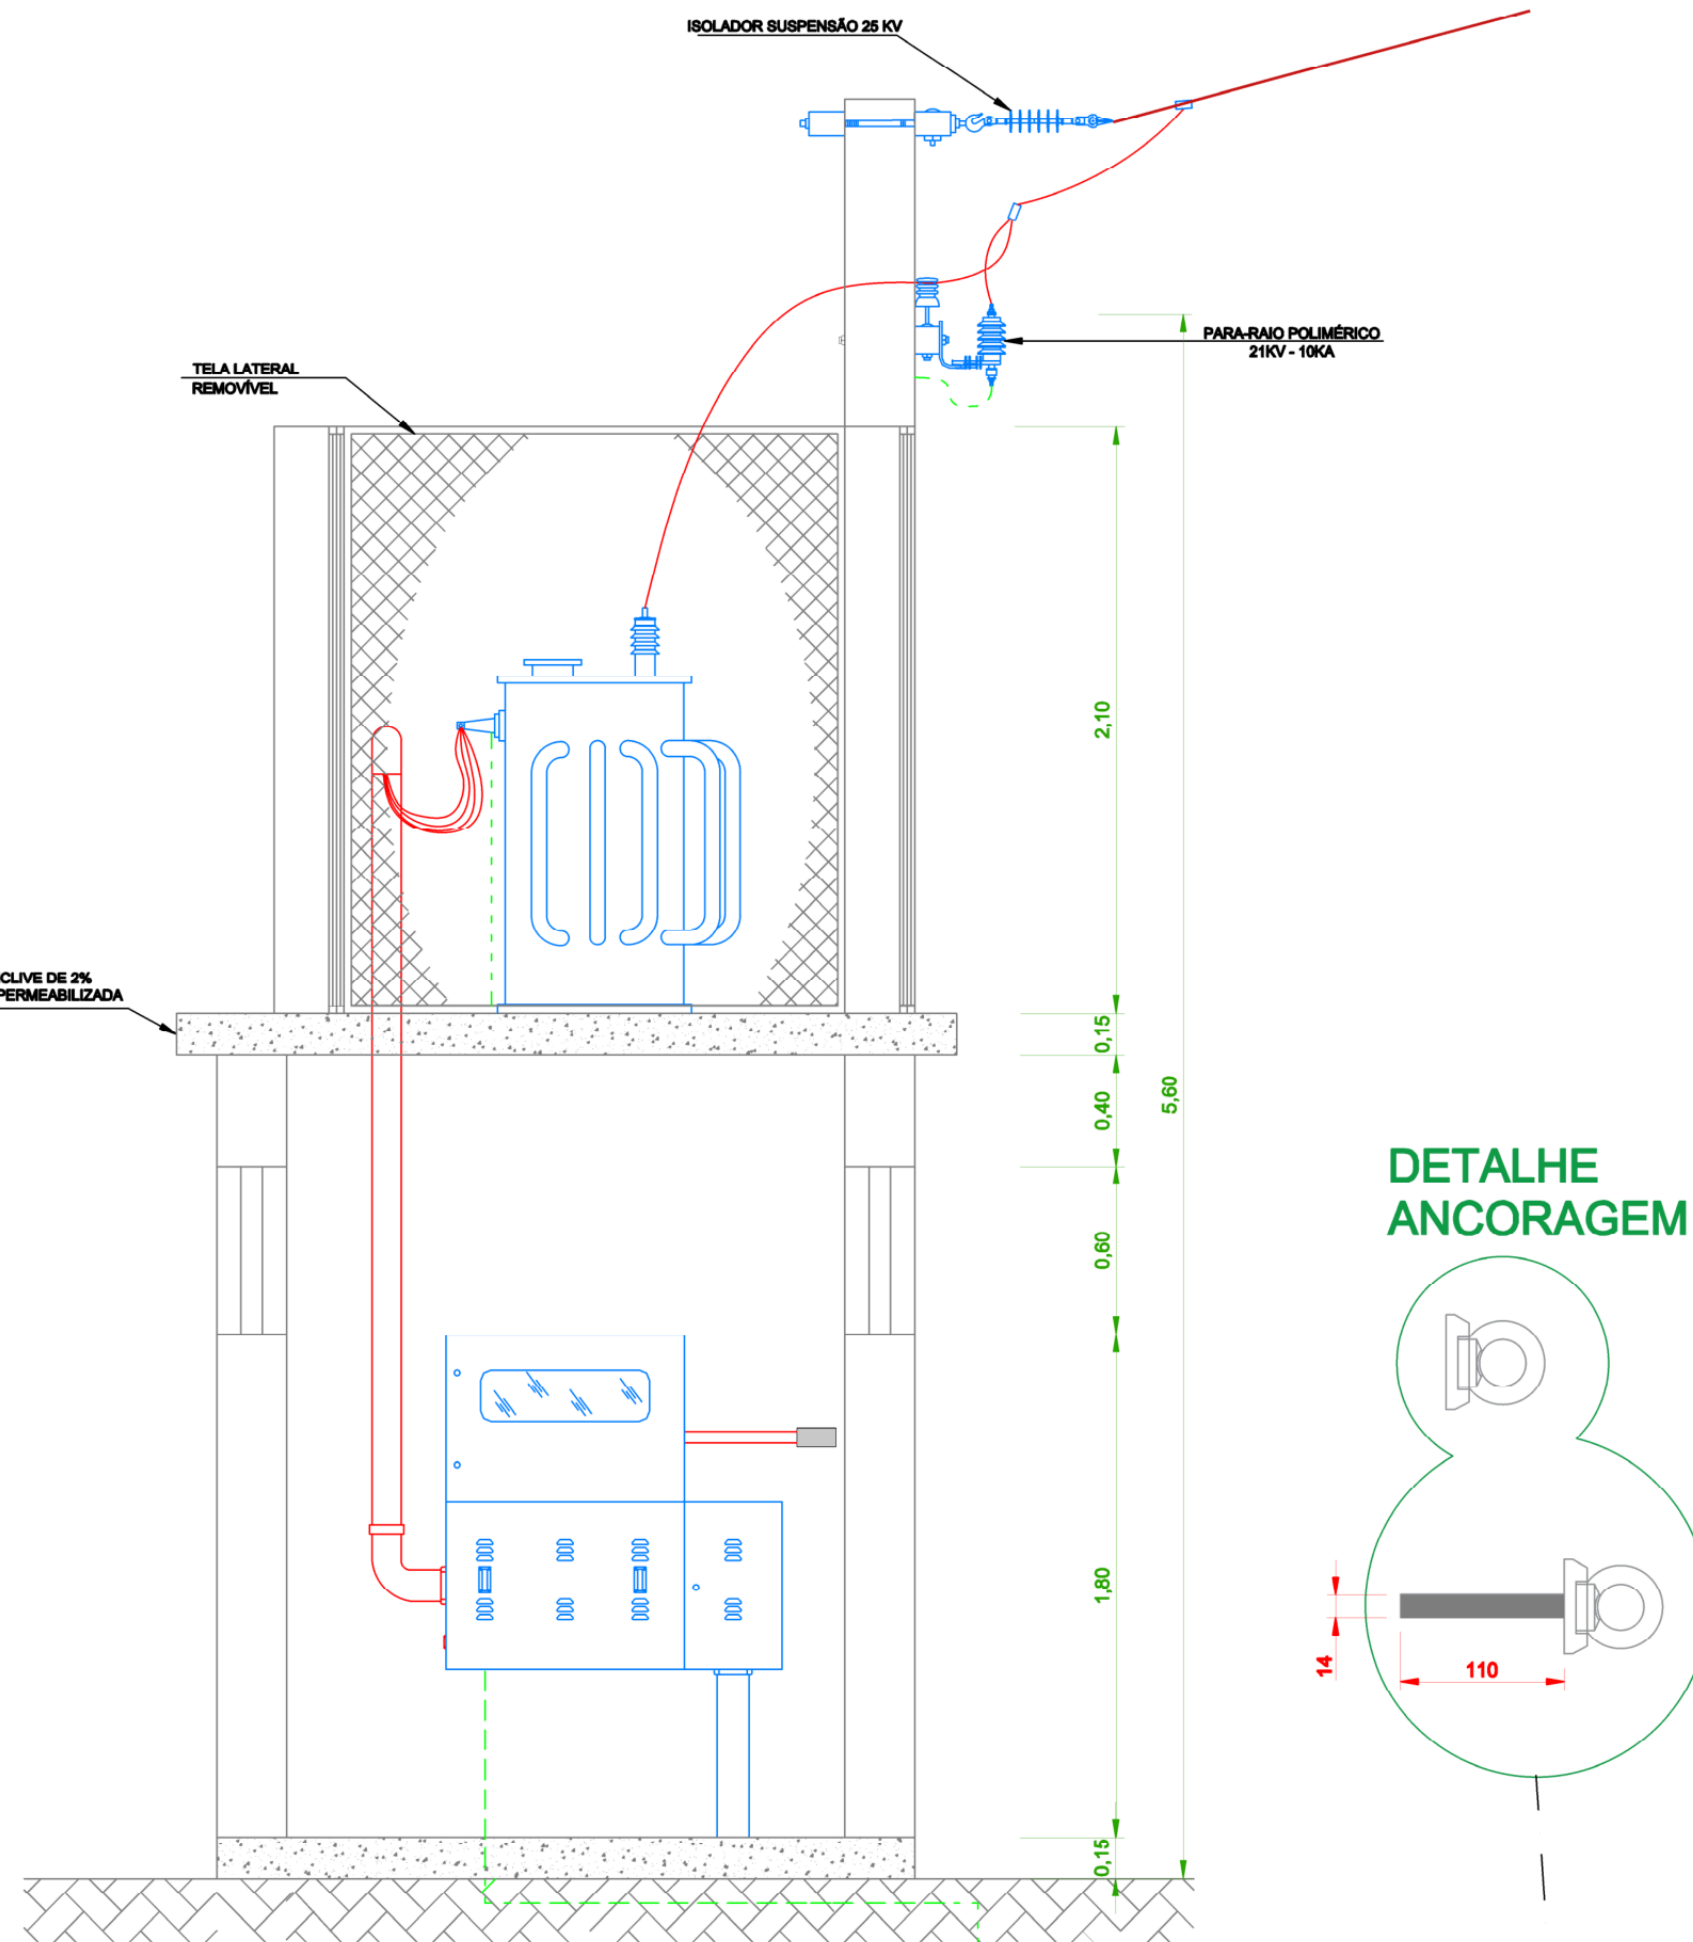

CORTE A - A'
ESCALA - 1:25

**DETALHE
ANCORAGEM**

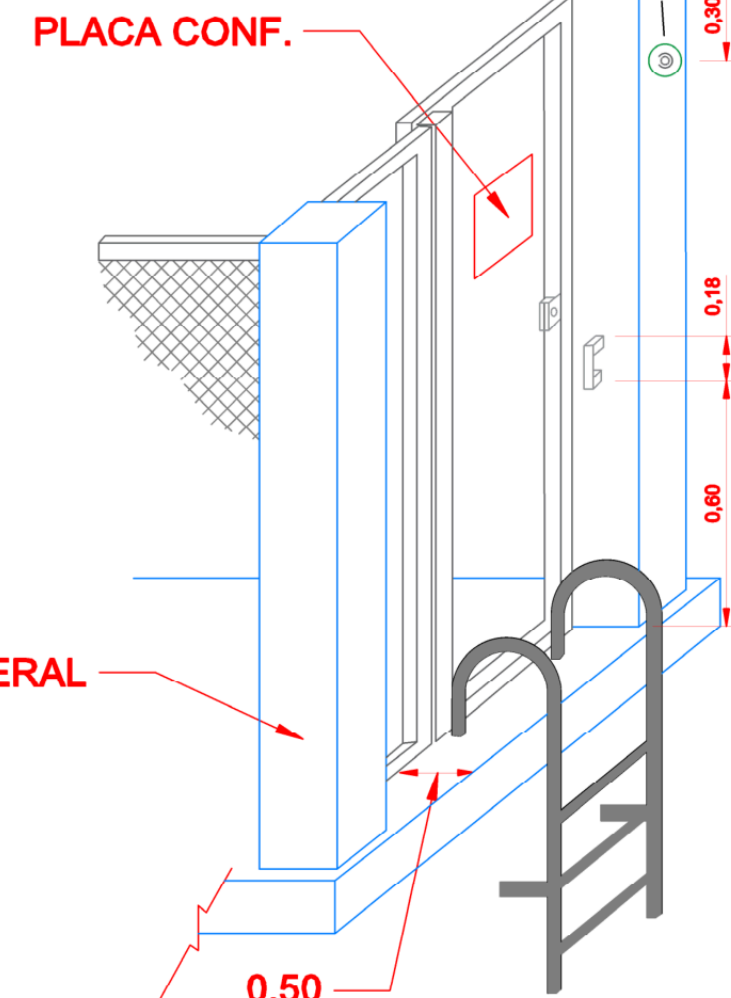

DETALHE DA ESCADA

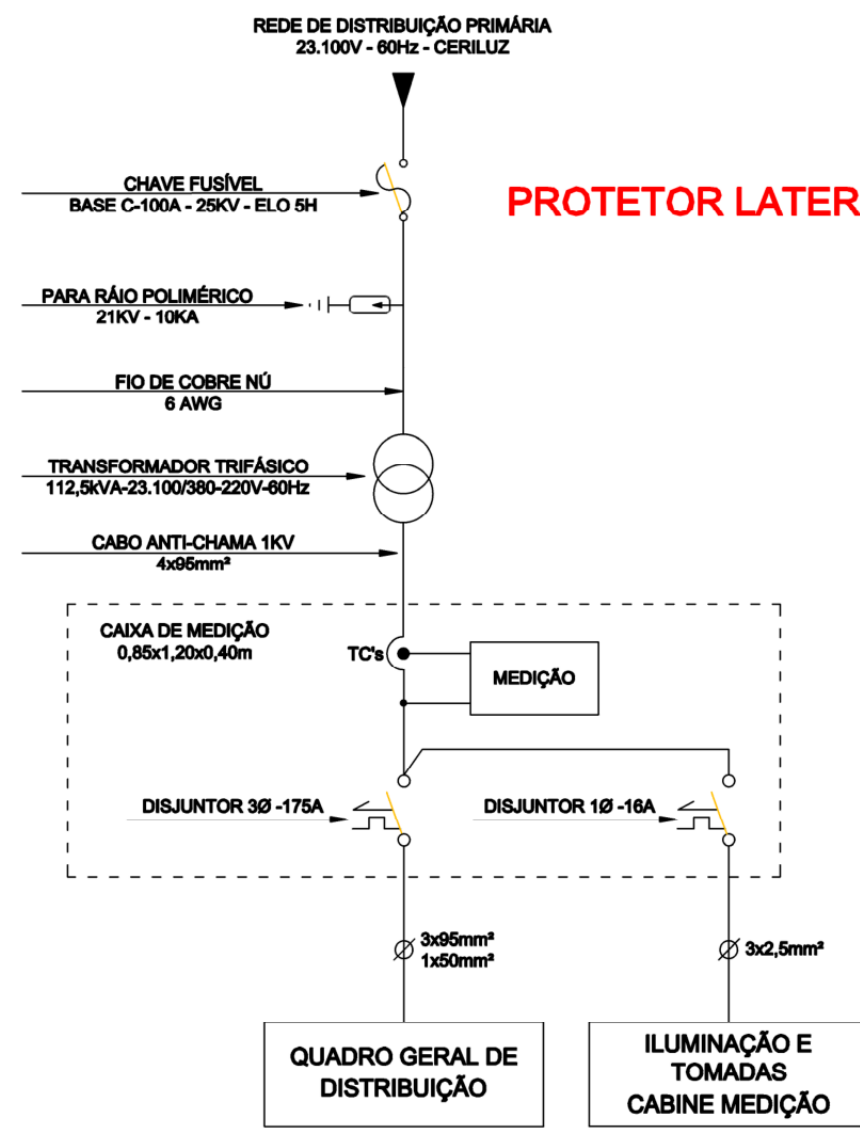


DIAGRAMA UNIFILAR

Nota de Precaução
Consultar o Manual Técnico
Descritivo p/ uma Perfil
Instalação

- NOTAS:**
- 1- AS JANELAS E A PORTA DEVEM SER METÁLICAS COM VENEZIANAS FIXAS.
 - 2- A PORTA DE ACESSO A MEDIÇÃO DEVE POSSUIR DISPOSITIVO PARA CADEADO OU FECHADURA PADRÃO DA COOPERATIVA.
 - 3- A LAJE DO 1º PAVIMENTO DEVE SUPORTAR NO MÍNIMO 2.500KG.
 - 4- A TELA DE PROTEÇÃO DEVE TER 2,10 DE ALTURA, SER DE ARAME Nº 14 BWG E DE MALHA DE 0,015 X 0,015 DO TIPO ÓTIS.
 - 5- AS CANTONEIRAS PARA FIXAÇÃO DAS TELAS DEVEM TER DIMENSÕES MÍNIMAS DE 50 X 50 X 6 mm.
 - 6- A RESISTÊNCIA MÁXIMA DA TERRA NÃO DEVE ULTRAPASSAR 10 OHMS EM QUALQUER ÉPOCA DO ANO.
 - 7- A MEDIÇÃO SERÁ INDIRETA EM BT.
 - 8- AS DIMENSÕES INDICADAS SÃO EM METROS.